


SUNNYDALE GAZEBO

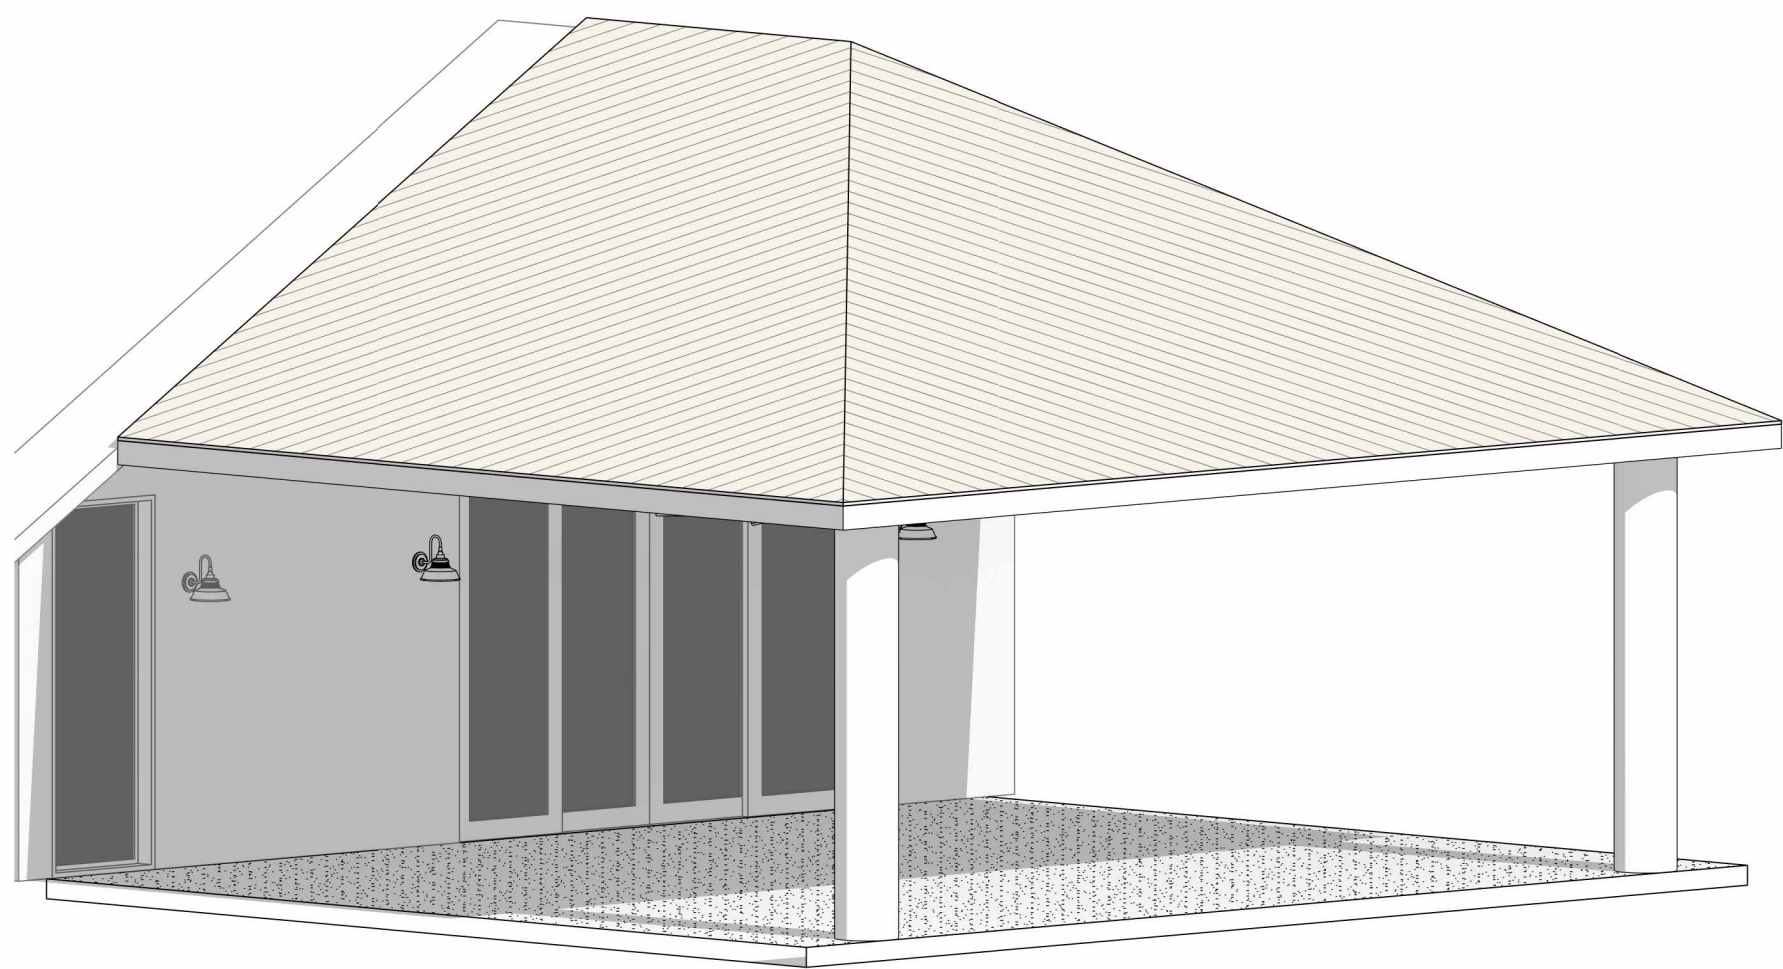


2 V2




3 SITE PLAN COVER
1" = 30'-0"

LOCATION MAP

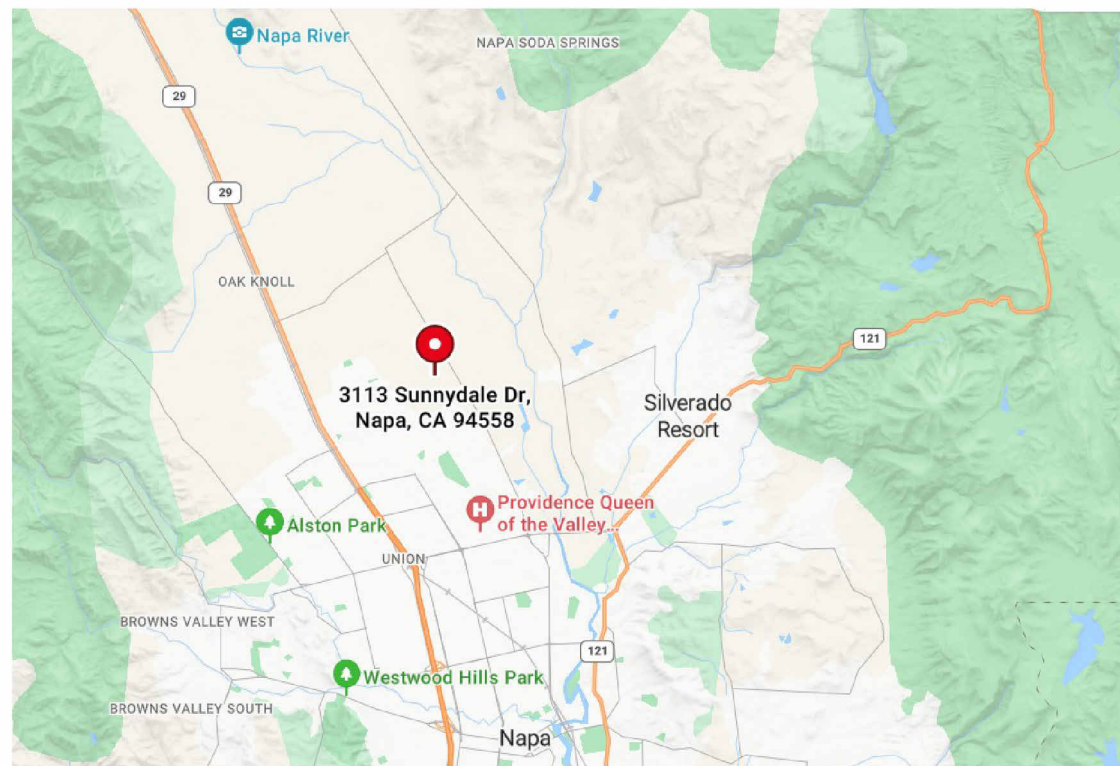

VICINITY MAP

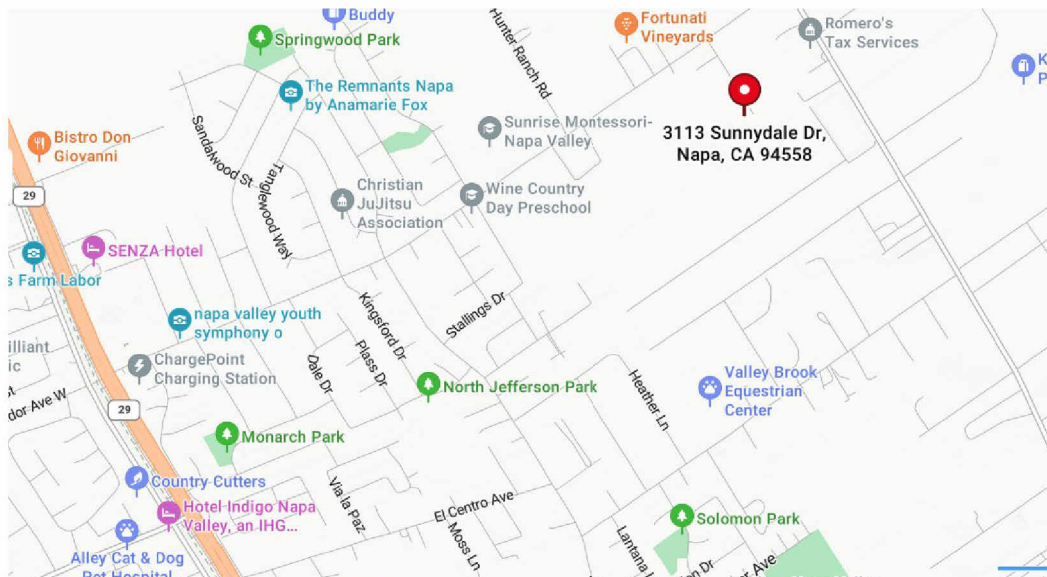

APPLICABLE CODES

CONSTRUCTION WILL COMPLY WITH THE FOLLOWING CODES AND ORDINANCES AS AMENDED BY THE STATE OF CALIFORNIA AND LOCAL JURISDICTION

2025 CALIFORNIA BUILDING CODE
2025 CALIFORNIA RESIDENTIAL CODE
2025 CALIFORNIA MECHANICAL CODE
2025 CALIFORNIA PLUMBING CODE
2025 CALIFORNIA ELECTRICAL CODE
2025 CALIFORNIA ENERGY CODE
2025 CALIFORNIA GREEN BUILDING STANDARDS
CALGREEN MANDATORY MEASURES: CHECKLIST
PROVIDED ON SHEETS CG1, CG2

2025 CALIFORNIA FIRE CODE (Title 24, Part 9)
2025 CALIFORNIA WILDLAND-URBAN INTERFACE
CODE (Title 24, Part 7)

NEW CONSTRUCTION SHALL COMPLY WITH THE 2025 CALIFORNIA WILDLAND-URBAN INTERFACE CODE (TITLE 24, PART 7) AND REQUIREMENTS SHOWN IN THE CALIFORNIA BUILDING CODE / RESIDENTIAL CODE SERIES (CBC/CRC)*
STRUCTURES LOCATED WITHIN 50 FEET FROM THE STRUCTURE SHALL COMPLY WITH THE WUI STANDARDS AND MEET WUI CONSTRUCTION REQUIREMENTS.

NAPA COUNTY NOTES

BUILDING CODES - THESE PLANS COMPLY WITH THE APPLICABLE SECTIONS OF THE 2025 ADOPTED EDITION OF THE CALIFORNIA BUILDING CODE / RESIDENTIAL CODE SERIES (CBC/CRC)

NCFD NOTES

THE NEAREST HYDRANTS SHALL BE POSTED AT PUBLIC ROADWAY AND AT ANY OTHER INTERSECTION OR RESIDENTIAL ROADWAY. HEIGHT OF NUMBERS SHALL BE A MINIMUM OF 4" HIGH ON A CONTRASTING BACKGROUND AND THE NUMBERS SHALL BE REFLECTIVE, AND MUST BE SEEN FROM BOTH DIRECTIONS OF TRAVEL. SEE DETAIL 1A OF THE NCFD STANDARDS.

PROJECT SHALL COMPLY WITH ALL THE REQUIREMENTS OF NAPA COUNTY DEFENSIBLE SPACE COMPLIANCE.

DEFENSIBLE SPACE FOR WILDFIRE SHALL BE A MINIMUM OF 100 FEET FROM ALL STRUCTURES. AROUND ALL PROPERTY LINES, GREATER CLEARANCE MAY BE REQUIRED UPON INSPECTION AS DETERMINED DUE TO SLOPE AND FUEL LOAD.

OVERHEAD CLEARANCE OF TREE LIMBS AND BRUSH ALONG THE ENTIRE LENGTH OF THE ACCESS ROADWAY SHALL BE A MINIMUM OF 13' 6" VERTICAL FT. SEE DETAIL 4 OF THE NCFD STANDARDS.

NCFD - DEFENSIBLE SPACE CLEARANCE SHALL BE 110 FEET OR CASE OF SITE FIRE PROXIMITY.

PROJECT SHALL COMPLY WITH 2025 FIRE CODE.

PROJECT CONTACTS

OWNER:
Paul & Megan Krsek
3113 Sunnydale Ln.
Napa, Ca 94558

CODE 360:
Damian Ostertag
Website: CodeHelpNapa.com
Cell: 707-637-7066

DESIGNER:
Scott Lunsford
PO BOX 30
COLUSA, CA 95932
530-216-5050
scott@outkastdesigns.com

ENGINEER:
CHRIS OLIVEIRA AND ASSOC.
SUITE 140-119
EL DORADO HILLS, CA 95762
916-933-6073
916-933-4731 FAX
chris0602@sbcglobal.net

PROJECT INFORMATION

SITE ADDRESS:
3113 SUNNYDALE DR
NAPA, CA 94558

APN:
038-050-009

ZONING:
AP

PARCEL SIZE:
.481 ACERS

SCOPE OF WORK

GAZEBO
618 SQ. FT. GAZEBO METAL WITH FR CLOTH ROOF COVER
Legalization of un permitted attached gazebo (618 SF) — steel frame, columns, slab, wall, attachment, and electrical lighting and heaters. Non-compliant fabric top replaced with NPS-701 / UP-616 fire-rated cover.

WILDLAND-URBAN INTERFACE AREA NOTES

WILDLAND-URBAN INTERFACE AREA: YES

COMPLY WITH THE REQUIREMENTS OF 2025 CRC SECTION R337, MATERIALS AND CONSTRUCTION METHODS FOR EXTERIOR WILDFIRE EXPOSURE. SEE [HTTP://OSM.FIRE.CA.GOV/BML.HTML](http://osm.fire.ca.gov/BML.html) FOR UPDATED INFORMATION.

- A. SPECIFY NON-COMBUSTIBLE OR IGNITION RESISTANT EXTERIOR WALL COVERINGS IN ACCORDANCE WITH 2025 CRC SECTION R337.7.
- B. SPECIFY EXTERIOR GLAZING IN ACCORDANCE WITH 2025 CRC SECTION R337.8. ONE PANE OF WINDOW SHALL ALSO BE TEMPERED.
- C. SPECIFY DECKING MATERIAL IN ACCORDANCE WITH 2025 CRC SECTION R337.9.
- D. SPECIFY IGNITION RESISTANT OR NON-COMBUSTIBLE EAVES AND SOFFITS IN ACCORDANCE WITH 2025 CRC SECTION R337.7.3. OPEN ROOF EAVES REQUIRE NON-COMBUSTIBLE OR IGNITION RESISTANT MATERIALS, SUCH AS FIRE-RESISTANT PLYWOOD OR OSB. REFER TO SIM WEB SITE ABOVE FOR APPROVED MATERIALS.
- E. SPECIFY FIRE RESISTIVE EXTERIOR DOORS IN ACCORDANCE WITH 2025 CRC SECTION R337.8. (THE DOOR EXTERIOR SURFACE SHALL BE OF NON-COMBUSTIBLE OR IGNITION-RESISTANT MATERIALS OR BE CONSTRUCTED OF SOLID CORE WOOD 1-3/8" THICK OR HAVE A FIRE-RESISTIVE RATING OF NOT LESS THAN 20 MINUTES.)
- F. SPECIFY IGNITION RESISTANT OR NON-COMBUSTIBLE EXTERIOR PORCH CEILINGS IN ACCORDANCE WITH 2025 CRC SECTION R337.7.6.
- G. SPECIFY THAT GABLE ATTIC VENTS AND FOUNDATION VENTS SHALL BE FULLY COVERED WITH METAL WIRE MESH OR NON-COMBUSTIBLE MATERIALS WITH MINIMUM OF 1/16" AND SHALL NOT EXCEED 1/8" OPENINGS IN COMPLIANCE WITH 2025 CRC SECTION R337.6.2.
- H. SPECIFY THE APPROVED EAVE VENTS THAT RESIST THE INTRUSION OF FLAME AND BURNING EMBERS. PER 2025 CRC SECTION R337.6.2. (E.G. VULCAN VENTS OR TESTED EQUIVALENT)
- I. SPECIFY THAT THE ROOF GUTTERS SHALL BE PROVIDED WITH MEANS TO PREVENT THE ACCUMULATION OF LEAVES AND DEBRIS IN THE GUTTER. 2025 CRC SECTION R337.5.4.



www.outkastdesigns.com

3113 SUNNYDALE



ENGINEER OF RECORD

BUILDING DEPARTMENT

COVER

APN 038-050-009

3113 Sunnydale Dr,
Napa Ca. 94558

Project Number 9795-26

Date 6-9-26


Drawn By SL

Outkast Designs | PO Box 30 | Colusa CA | 95932 | scott@outkastdesigns.com

A01

Scale As indicated

7/15/2026 4:41:20 PM

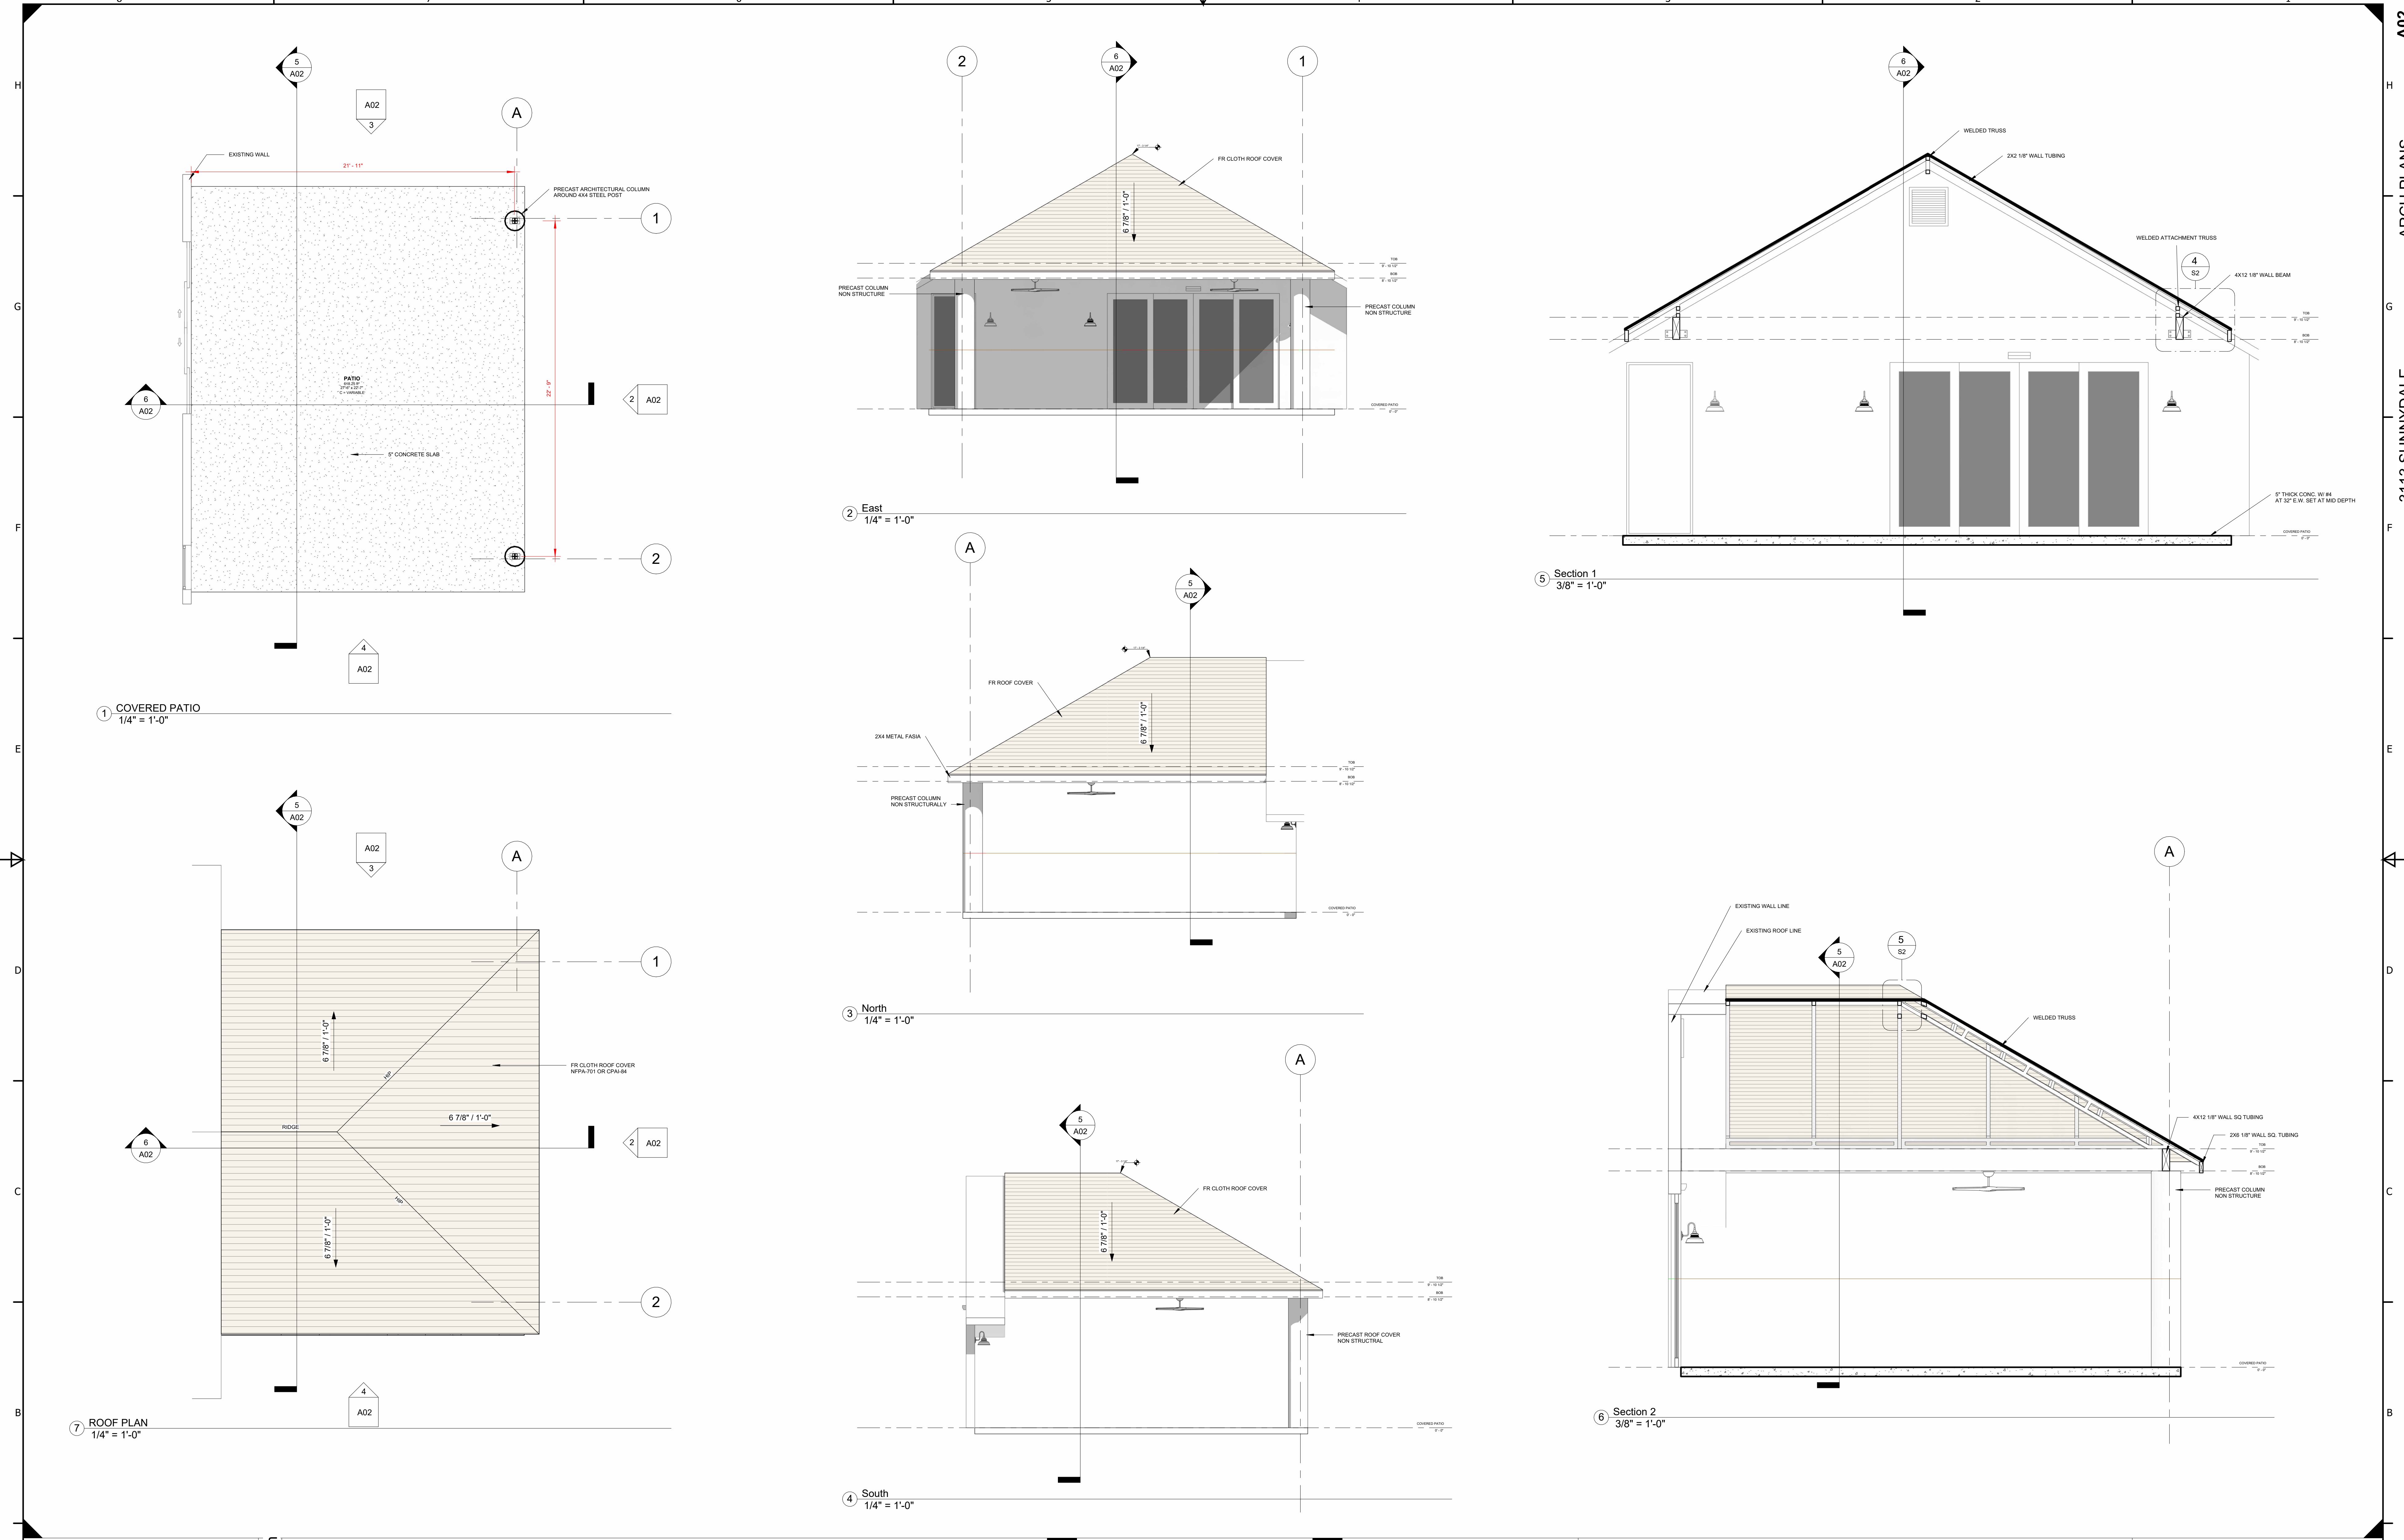



www.outkastdesigns.com

3113 SUNNYDALE



MEMBER
A I B D
AMERICAN INSTITUTE OF BUILDING DESIGNERS

ENGINEER OF RECORD


BUILDING DEPARTMENT

ARCH PLANS	
APN 038-050-009	Project Number 9795-26
3113 Sunnydale Dr, Napa Ca. 94558	Date 6-9-26
	Drawn By <i>Scott</i> SL
	Outkast Designs PO Box 301 Colusa CA 95632 scott@outkastdesigns.com

A02

Scale As indicated

7/15/2026 4:41:26 PM

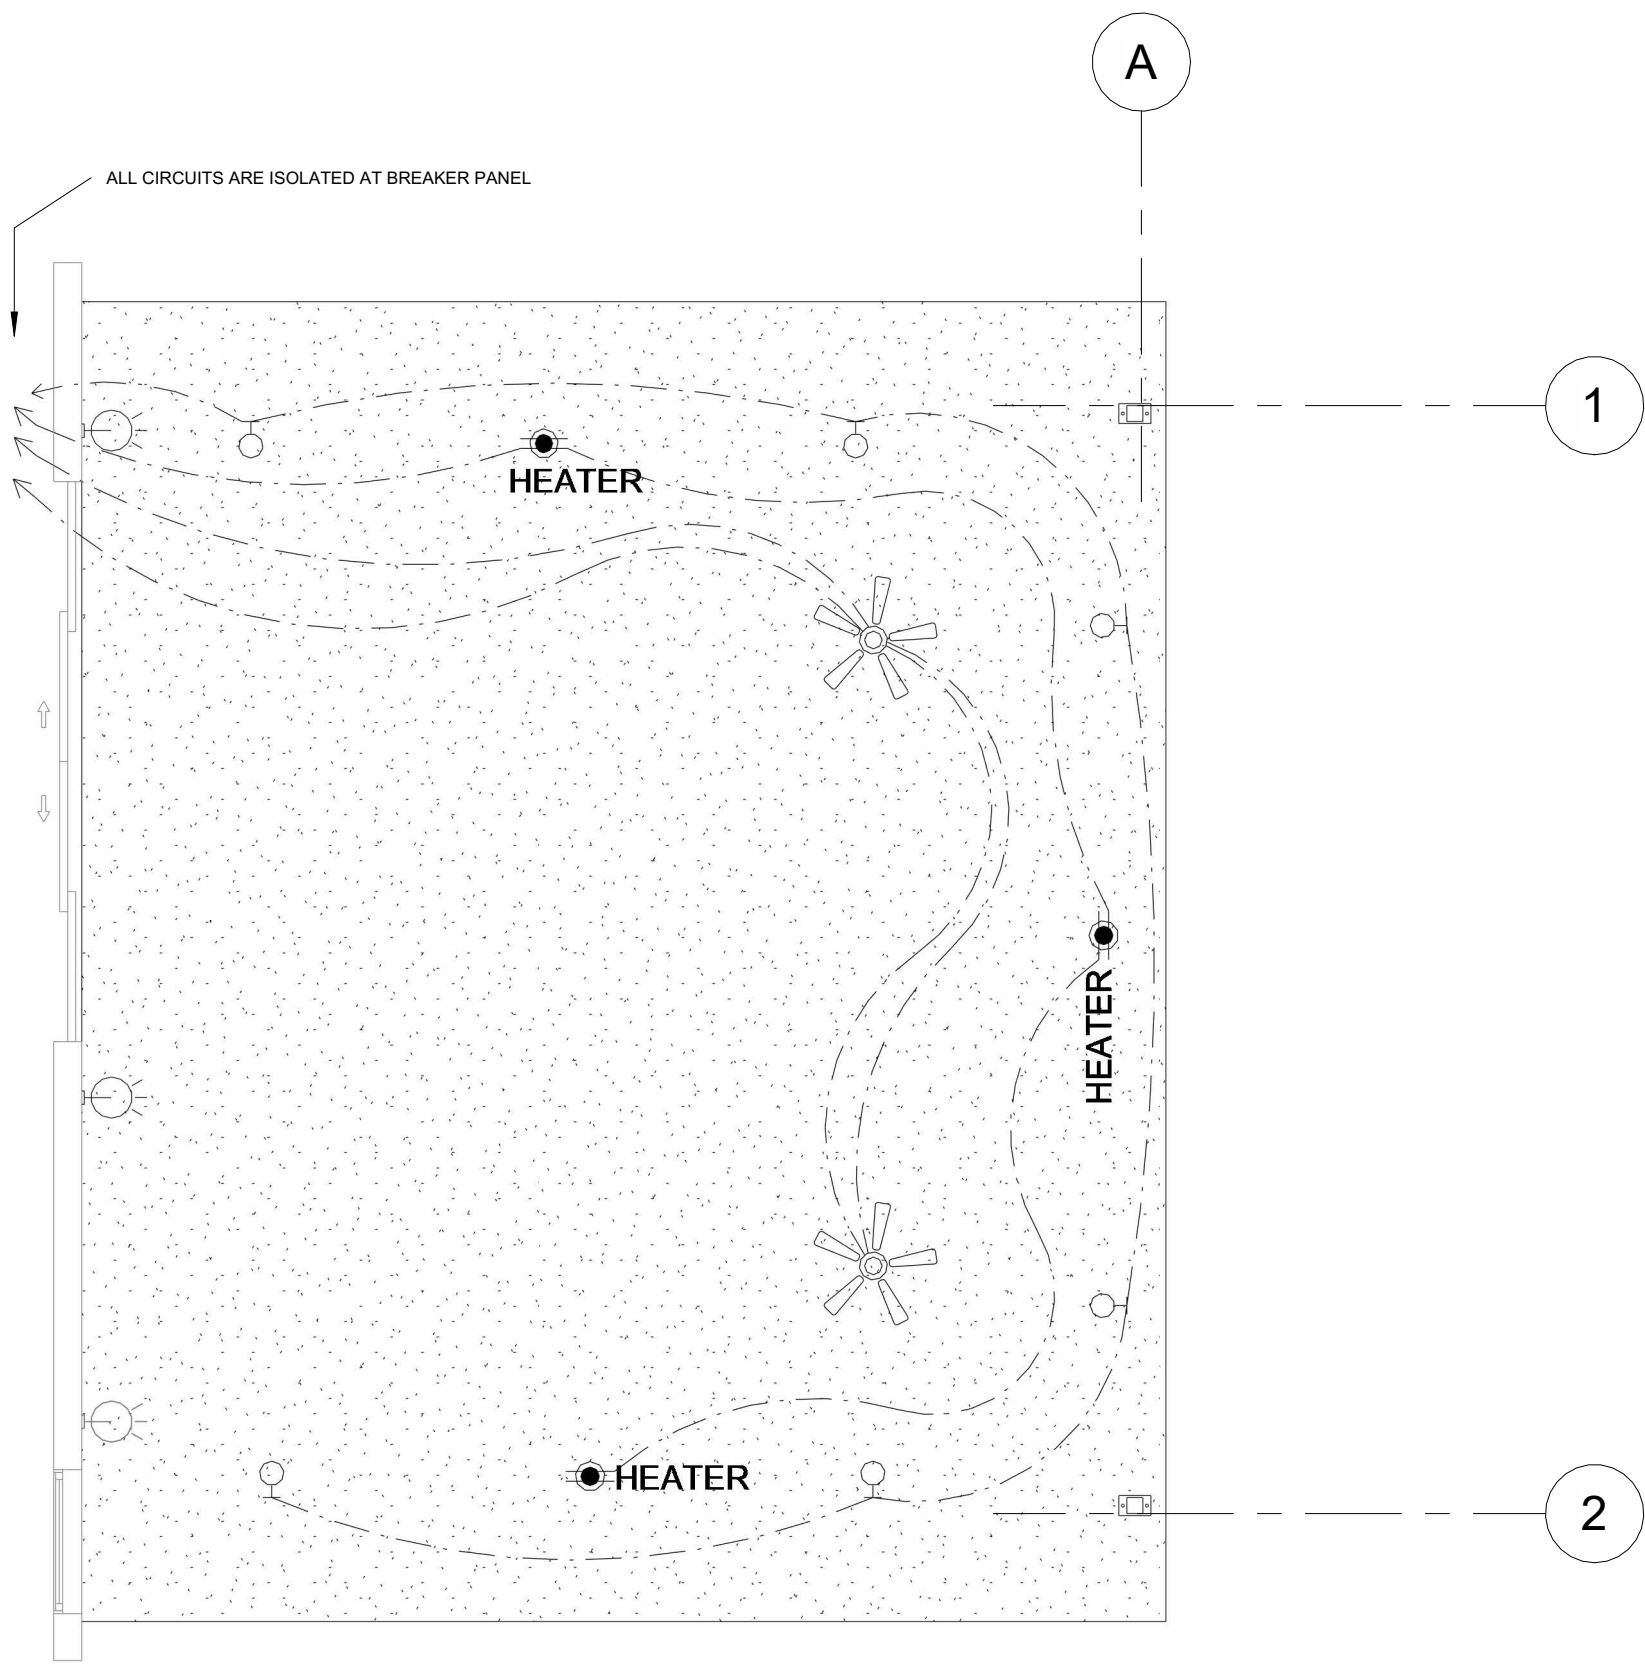

ELECTRICAL LEGEND

OUTLETS

WP/GF1 DUPLEX OUTLET CEILING MOUNTED

CLIMATE CONTROL

CEILING FAN

LIGHTING

WALL MOUNTED EXTERIOR LIGHT FIXTURE

1 ELECTRICAL PLAN
1/4" = 1'-0"



www.outkastdesigns.com



3113 SUNNYDALE



ENGINEER OF RECORD

BUILDING DEPARTMENT

ELECTRICAL PLAN

APN 038-050-009	Project Number	9795-26
3113 Sunnydale Dr, Napa Ca. 94558	Date	6-9-26
	Drawn By	SL
	OutKast Designs PO Box 301 Colusa CA 95932 scott@outkastdesigns.com	

Scale As indicated

E1

STRUCTURAL NOTES:

GENERAL NOTES:

- ALL CONSTRUCTION SHALL COMPLY WITH THE LATEST EDITION OF THE INTERNATIONAL BUILDING CODE , APPLICABLE STANDARDS, AND THE 2025 CBC
- THE CONTRACTOR SHALL BE RESPONSIBLE FOR THE SAFETY OF THE BUILDING DURING CONSTRUCTION AND SHALL PROVIDE ADEQUATE SHORING AND BRACING DURING CONSTRUCTION. CONTRACTOR SHALL COMPLY WITH APPLICABLE SAFETY REGULATIONS.
- DETAILS NOT SPECIFICALLY SHOWN SHALL BE SIMILAR TO DETAILS FOR SIMILAR CONSTRUCTION SHOWN ON THESE DRAWINGS.
- THE CONTRACTOR SHALL COORDINATE THE WORK OF ALL TRADES AND SHALL CHECK ALL DIMENSIONS. ANY DISCREPANCIES SHALL BE CALLED TO THE ATTENTION OF THE ENGINEER AND BE RESOLVED BEFORE PROCEEDING WITH THE WORK.
- NO STRUCTURAL MEMBERS SHALL BE CUT, NOTCHED OR OTHERWISE PENETRATED UNLESS SPECIFICALLY APPROVED BY THE ENGINEER IN ADVANCE OR SHOWN ON THESE DRAWINGS.
- TYPICAL DETAILS SHALL APPLY UNLESS SHOWN OTHERWISE ON THE DRAWINGS.
- WHERE THESE GENERAL NOTES AND TYPICAL DETAILS ARE IN CONFLICT WITH ANY SPECIFICATIONS, THESE NOTES SHALL GOVERN.
- PROVIDE OPENINGS, CURBS, FRAMING AND/OR SUPPORTS FOR ITEMS INDICATED ON ANY OF THESE DRAWINGS INCLUDED IN THE CONSTRUCTION DOCUMENTS.
- ALL ELEVATIONS ARE REFERENCED FROM TOP OF FINISH GROUND FLOOR ELEVATION =0'-0" UNLESS OTHERWISE NOTED.
- PROVIDE INSPECTIONS IN AS REQUIRED BY THE BUILDING DEPT. OR THESE DRAWINGS.
- CONTRACTOR OR OWNER IS RESPONSIBLE FOR THE INSTALLATION AND SHALL PROVIDE PROPER FUNCTION OF ALL COSMETIC TREATMENTS AND FINISHES - INCLUDING, BUT NOT LIMITED TO: TILE, STUCCO, GYPSUM BOARD, PAINT, ETC. WHERE STANDARD SPECIFICATIONS CALL FOR CONSTRUCTION MORE STRINGENT THAN SHOWN ON THESE PLANS, THE CONTRACTOR OR OWNER SHALL ADJUST THE CONSTRUCTION ACCORDINGLY.
- CONTRACTOR SHALL READ AND BE FAMILIAR WITH ALL FACETS OF THE PLANS AND SPECIFICATIONS AND SHALL REQUEST CLARIFICATION AS REQUIRED BEFORE COMMENCING CONSTRUCTION. IF THESE PLANS ARE NOT EXECUTED BY A CONTRACTOR LICENSED IN CALIFORNIA AND WHO IS INTIMATELY FAMILIAR WITH THIS TYPE OF CONSTRUCTION, THE PLANS SHALL BE CONSIDERED NULL AND VOID.
- CONTRACTOR SHALL BE RESPONSIBLE FOR ANY CONSTRUCTION WHICH IS IN DEVIATION FROM THESE PLANS.
- CONTRACTOR SHALL NOTIFY THE ENGINEER OF ANY DISCREPANCIES BETWEEN PLANS AND ACTUAL FIELD CONDITIONS AND SHALL OBTAIN APPROVAL BEFORE CONTINUING CONSTRUCTION.
- CONTRACTOR IS RESPONSIBLE FOR THE CORRECT INSTALLATION OF ALL MANUFACTURED PRODUCTS, INCLUDING BUT NOT LIMITED TO OSB, T1-11 PARALLAMS AND MICRO-LAMS. ALL INSTALLATIONS SHALL BE DONE IN ACCORDANCE WITH MANUFACTURER'S SPECIFICATIONS

FOUNDATION:

- FOUNDATION SOIL STRATA IS NATIVE SOIL OR ENGINEERED FILL AS PER THE PROJECT SOILS REPORT WHEN APPLICABLE. IF ANY DISCREPANCIES EXIST BETWEEN THE SOILS REPORT & THESE PLANS, THE SOILS REPORT SHALL GOVERN.
SOILS REPORT:
WHEN NO SOILS REPORT IS AVAILABLE, IT IS THE RESPONSIBILITY OF THE CONTRACTOR AND/OR OWNER TO ENSURE THAT ALL SOIL CONDITIONS ARE APPROPRIATE FOR THE CONSTRUCTION OF THIS PROJECT AS DRAWN. FOUNDATIONS SHALL BEAR ON FIRM, UNDISTURBED FOUNDATION SOIL STRATA.
SOIL BEARING — 1500 pcf
(presumptive per CBC Table 1906.2, Class 4).
- THE ELEVATIONS OF BOTTOMS OF FOOTINGS AS SHOWN ON THESE DRAWINGS INDICATE THE ESTIMATED MINIMUM FOUNDATION DEPTHS.
- FOUNDATIONS ARE DESIGNED FOR A MAXIMUM DEAD PLUS LIVE LOAD ALLOWABLE SOIL BEARING PRESSURE OF 1500 PSF.
- BOTTOMS OF FOOTINGS SHALL EXTEND A MINIMUM OF 12" BELOW LOWEST ADJACENT GRADE FOR ONE STORY SECTIONS, 18" FOR TWO STORIES (U.O.N.)
- THE BOTTOM OF ALL FOOTINGS SHALL BE LEVEL. CHANGES IN FOOTING ELEVATIONS SHALL BE MADE UTILIZING THE TYPICAL FOOTING STEP DETAIL ON THESE DRAWINGS.
- CENTER FOOTINGS UNDER WALLS OR COLUMNS UNLESS OTHERWISE INDICATED ON THESE DRAWINGS.
- BOLTS AND NAILS IN CONTACT WITH PRESSURE TREATED WOOD SHALL BE HOT DIPPED ZINC COATED GALVANIZED OR EQ.

DESIGN CRITERIA:

RISK CATEGORY - II
IMPORTANCE FACTOR: 1
WIND SPEED: 110 MPH
EXPOSURE CATEGORY: B
INTERNAL PRESSURE COEFFICIENT: .18+/-
DESIGN WIND PRESSURE: SEE CALCS
MAPPED SPECTRAL RESPONSE COEFFICIENTS:
SITE CLASS: D
SPECTRAL RESPONSE COEFFICIENTS:
SEISMIC DESIGN CATEGORY: D
BASIC SEISMIC FORCE-RESISTING SYSTEM: WOOD SHEARWALLS
DESIGN BASE SHEAR: SEE CALCS
SEISMIC RESPONSE COEFFICIENT: C=0.118
SEISMIC R=6.5
ANALYSIS PROCEDURE: ELFP


ROOF D.L.: 22
ROOF LIVE LOAD: 20
SOLAR WT = 3 PSF

RAIN LOAD: 0
FLOOD LOAD: 0
SNOW LOAD: 0

S = 1.39
DS


CONCRETE:

- CONCRETE SHALL DEVELOP A MINIMUM ULTIMATE COMPRESSIVE STRENGTH OF 2500 PSI AT 28 DAYS IN ACCORDANCE WITH ASTM C39. ALL CONCRETE SHALL BE CONSOLIDATED BY MECHANICAL VIBRATORS.
- ALL CONCRETE WORK SHALL CONFORM TO THE REQUIREMENTS OF THE C.B.C. AND ACI STANDARD 318, LATEST EDITION, OF THE AMERICAN CONCRETE INSTITUTE UNLESS SHOWN OR NOTED OTHERWISE ON THESE DRAWINGS.
- AGGREGATE SHALL CONFORM TO ASTM C-33.
- CEMENT SHALL BE ASTM C-150, TYPE I OR TYPE II.
- REINFORCING STEEL SHALL BE DEFORMED CONFORMING TO ASTM A615 GRADE 40 FOR #5 AND SMALLER AND GR 60 FOR LARGER UNLESS OTHERWISE NOTED.
- WELDED WIRE FABRIC REINFORCEMENT SHALL CONFORM TO ASTM A-185.
- WELDING OF REINFORCING STEEL SHALL BE PERFORMED ONLY WHERE INDICATED ON THE DRAWINGS AND SHALL BE IN COMPLIANCE WITH ALL REQUIREMENTS OF THE REINFORCING STEEL WELDING SOCIETY. PROVIDE WELDING PROCEDURE AND MILL TEST REPORTS FOR ALL REINFORCEMENT TO BE WELDED. ENGINEER SHALL APPROVE WELDING PROCEDURE AND MILL TEST REPORTS PRIOR TO EXECUTION OF WELDING.
- COVERAGE FOR REINFORCING BARS SHALL BE IN ACCORDANCE WITH THE REQUIREMENTS OF THE C.B.C. AND ACI STANDARD 318 UNLESS SHOWN OTHERWISE ON THE DRAWINGS.
- LAP SPLICES FOR REINFORCING SHALL BE 50 BAR DIAMETERS OR 12" MINIMUM UNLESS SHOWN OTHERWISE ON THE DRAWINGS. WIRE BARS TOGETHER AT LAPS OR SPLICES, HOOKS SHALL BE 135 DEGREES WITH 4" MIN TAILS
- CONCRETE SHALL BE PLACED IN ACCORDANCE WITH ASTM C94 AND ACI STANDARD 304.
- ALL EMBEDDED ITEMS SHALL BE PLACED ACCURATELY AND SECURELY PRIOR TO BEGINNING CONCRETE PLACEMENT.
- CONSTRUCTION JOINTS SHALL BE LOCATED SO AS NOT TO IMPAIR THE STRENGTH OF THE STRUCTURE.
- MEETING COMPRESSIVE STRENGTH REQUIREMENTS ARE THE RESPONSIBILITY OF THE CONCRETE SUPPLIER
- SUBMIT CONCRETE MIX DESIGNS TO THE ENGINEER FOR APPROVAL PRIOR TO PLACEMENT OF ANY CONCRETE.
- ALL GROUT SHALL BE NON-METALLIC NON-SHRINK GROUT
- REINFORCING AND EMBEDMENT ITEMS SHALL BE FREE OF EXCESSIVE SCALE OR RUST, DIRT, GREASE, OIL OR ANY OTHER SUBSTANCE THAT WILL IMPAIR BOND WITH CONCRETE.
- NO SPECIAL INSPECTION IS REQUIRED.
- BOLTS AND NAILS IN CONTACT WITH PRESSURE TREATED WOOD SHALL BE HOT DIPPED ZINC COATED GALVANIZED OR EQ.

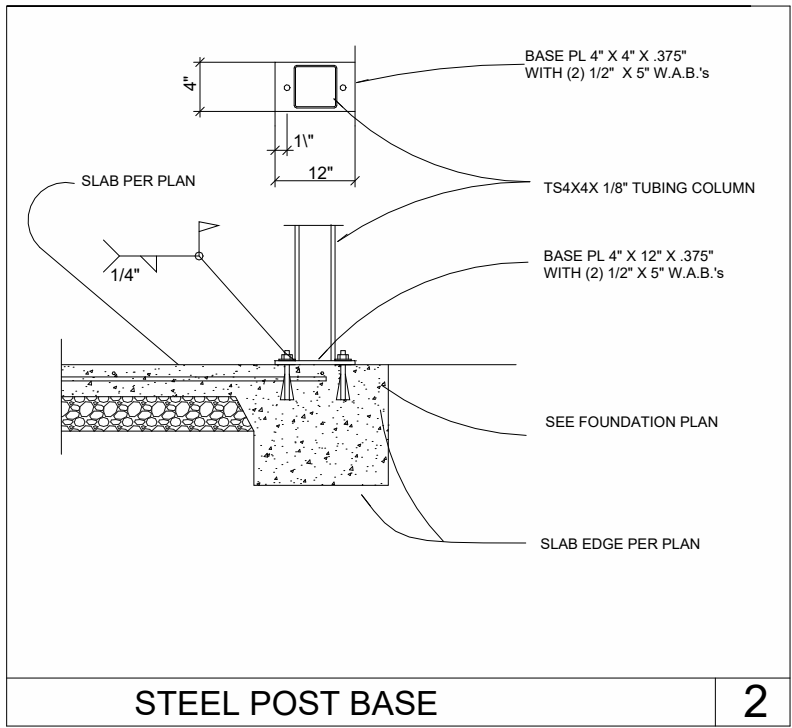

2 ENG POST BASE
1/8" = 1'-0"

REVISIONS

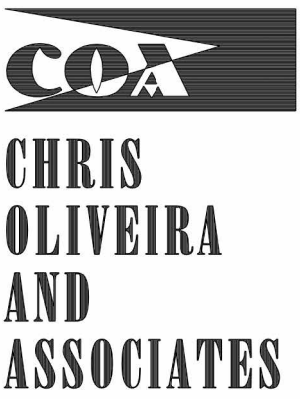

General Notes
and Details

DATE

SCALE

DRAWN

JOB

SHEET

SD1

OF

GENERAL NOTES & DETAILS

APN 038-050-009

3113 Sunnydale Dr,
Napa Ca. 94558

Project Number

9795-26

Date

6-9-26

Drawn By

SL

OutKast Designs | PO Box 301 | Colusa CA | 95632 | scott@outkastdesigns.com

SD1

Scale

As indicated

1 SD1 SHEET
1/4" = 1'-0"




www.outkastdesigns.com



3113 SUNNYDALE




ENGINEER OF RECORD

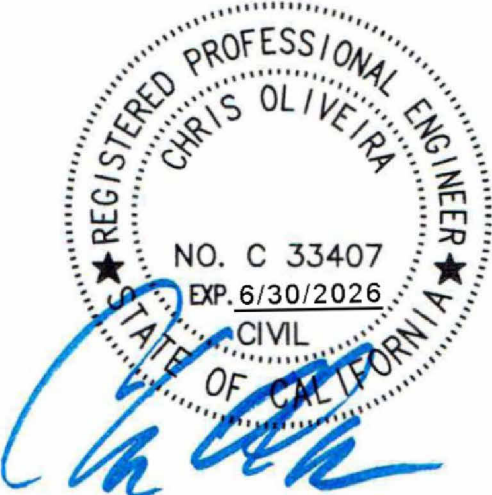


BUILDING DEPARTMENT

7/15/2026 4:41:38 PM

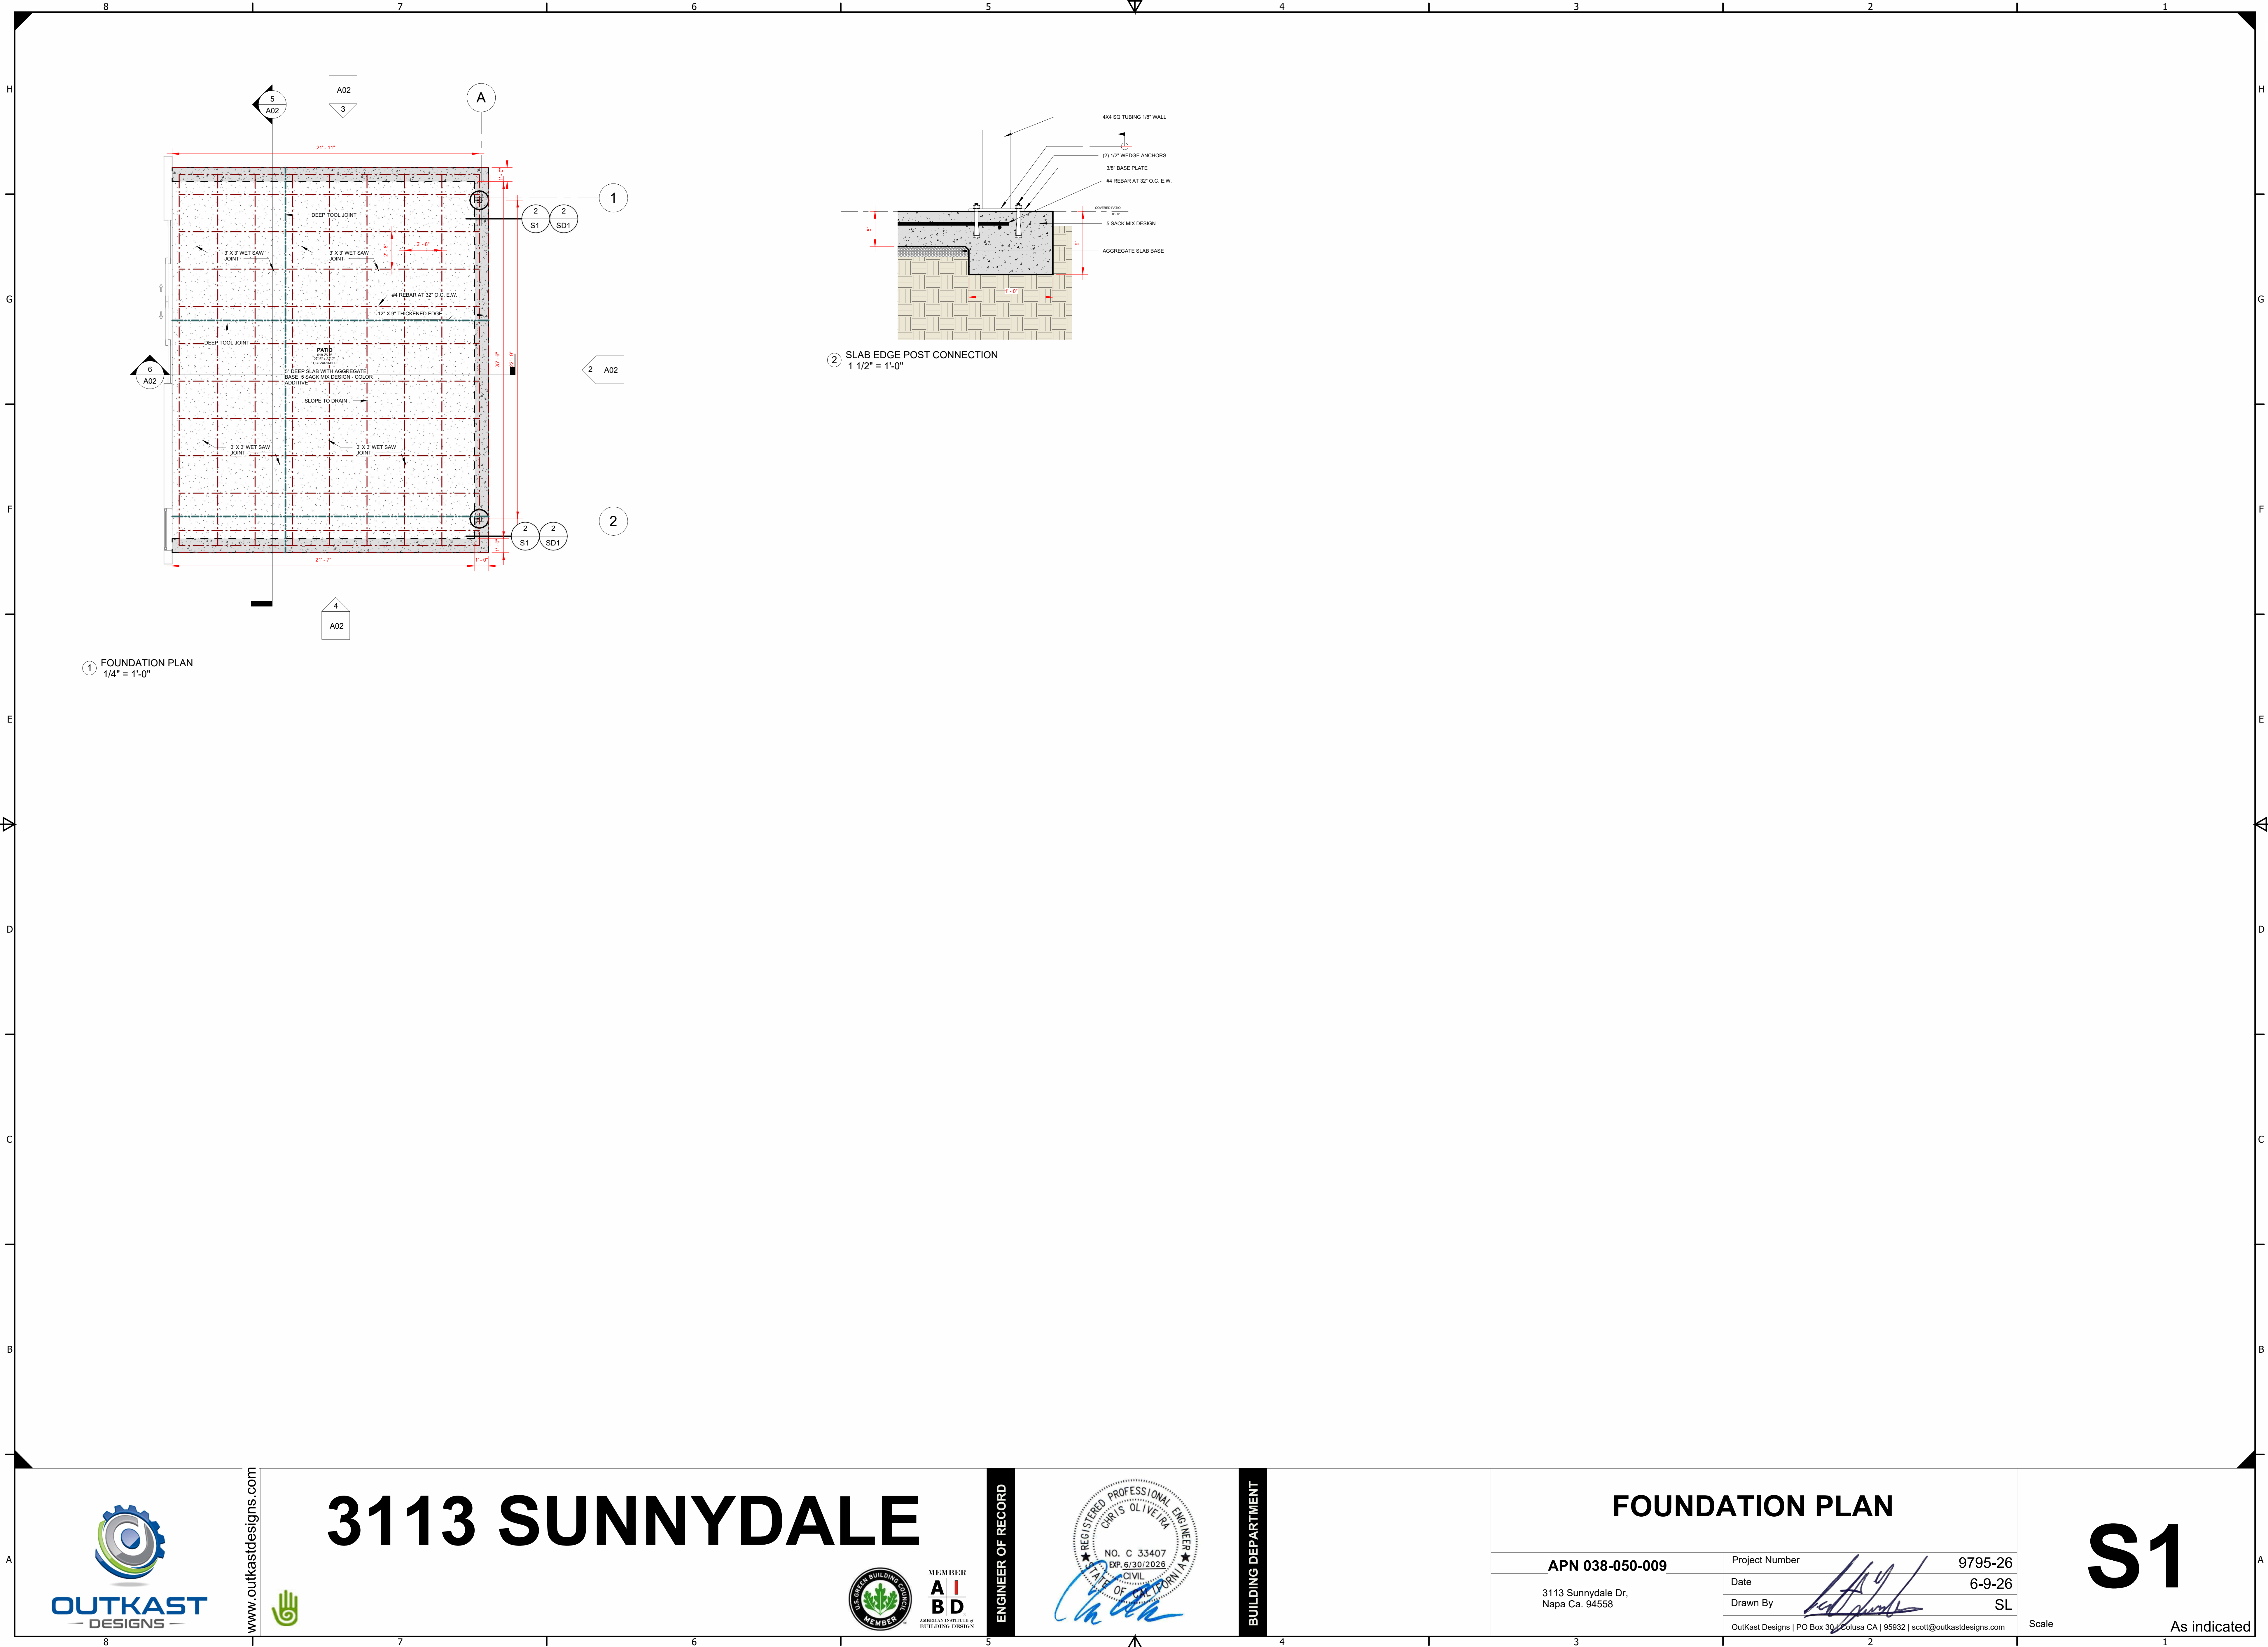

3113 SUNNYDALE

ENGINEER OF RECORD

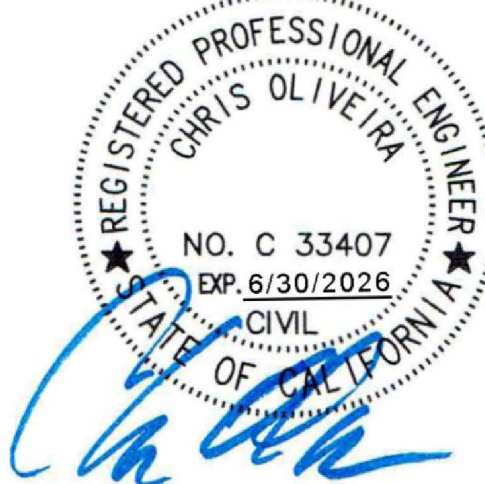



BUILDING DEPARTMENT

FOUNDATION PLAN

APN 038-050-009 3113 Sunnydale Dr, Napa Ca. 94558	Project Number	9795-26
	Date	6-9-26
	Drawn By	SL
	OutKast Designs PO Box 301 Colusa CA 95932 scott@outkastdesigns.com	

Scale As indicated

S1

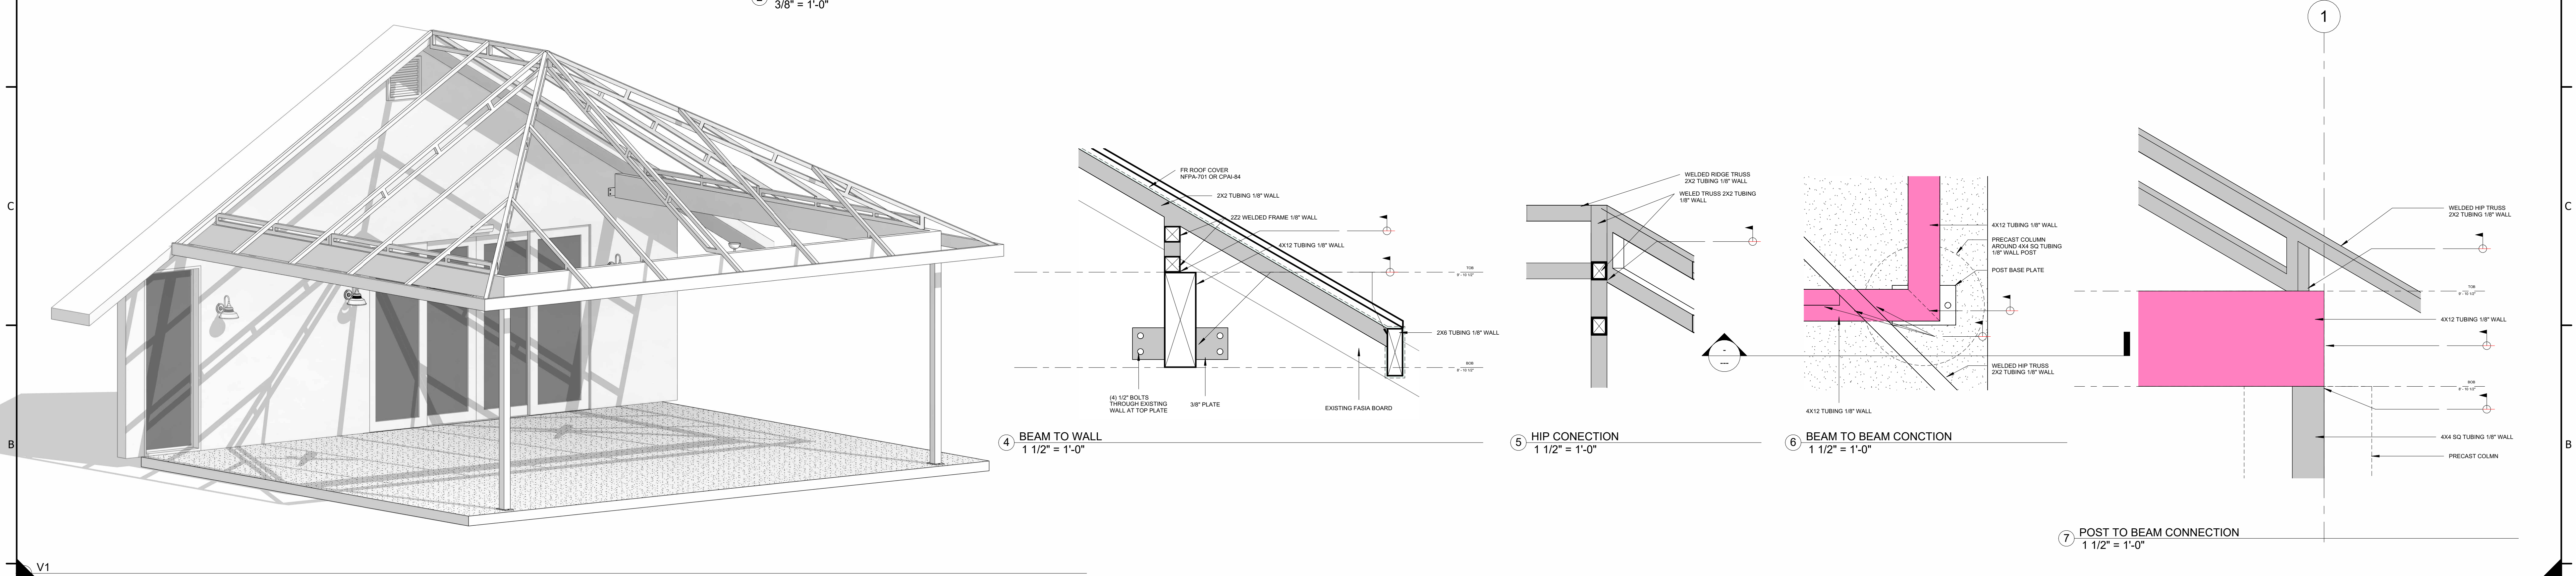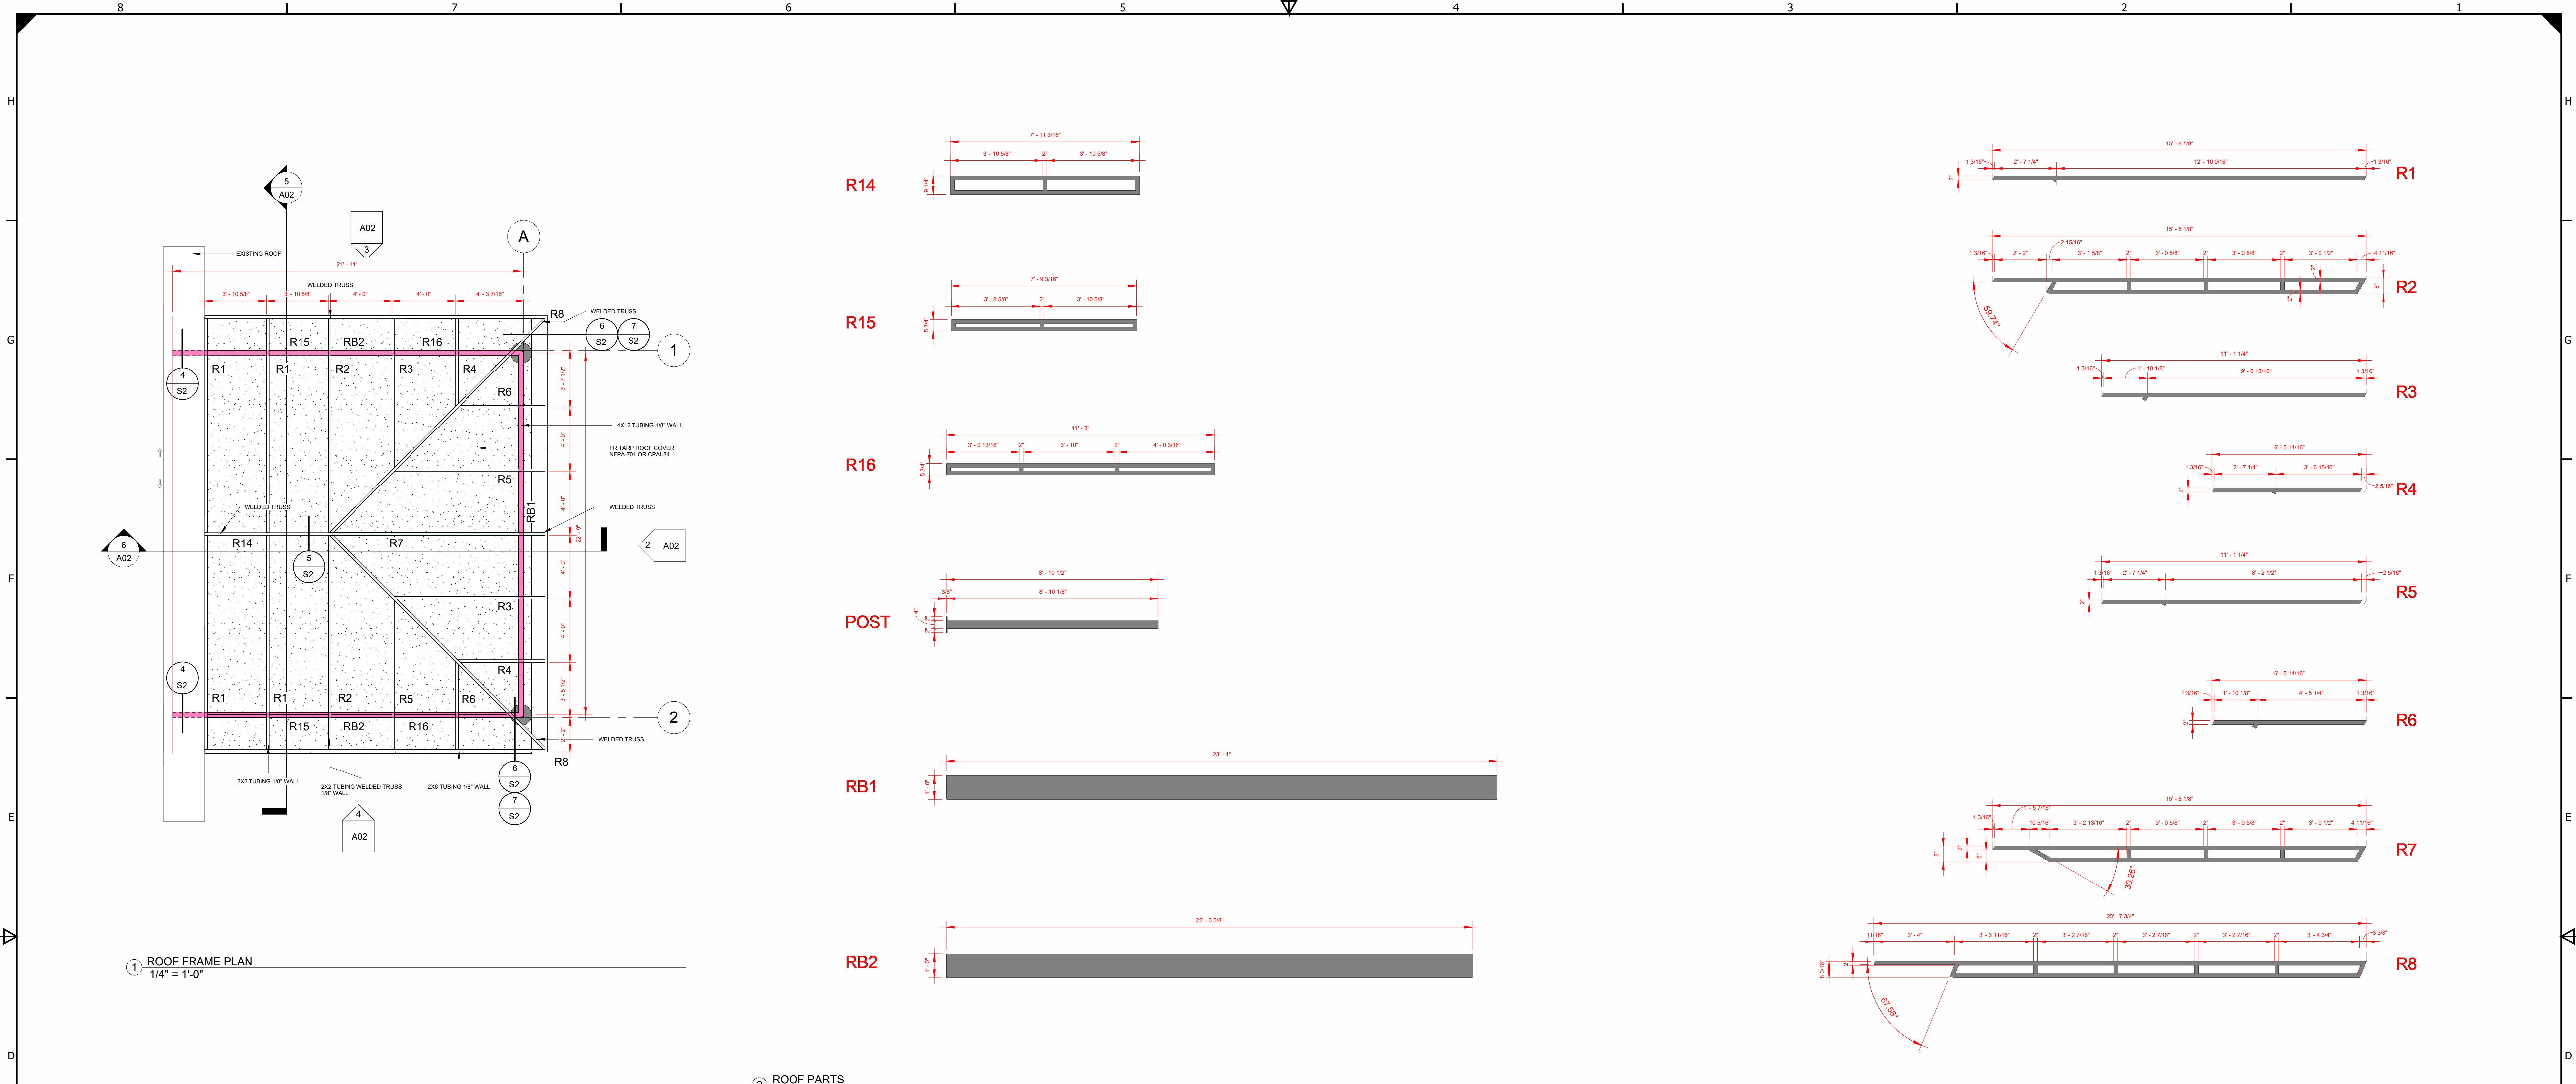




www.outkastdesigns.com

3113 SUNNYDALE



MEMBER
A I B D
AMERICAN INSTITUTE OF BUILDING DESIGNERS

ENGINEER OF RECORD

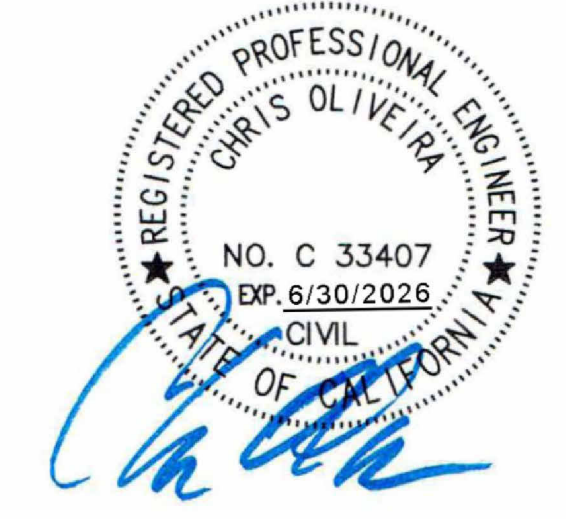

REGISTERED PROFESSIONAL ENGINEER
CHRIS OLIVEIRA
NO. C 33407
EXP. 8/30/2026
CIVIL
STATE OF CALIFORNIA

BUILDING DEPARTMENT


ROOF LAYOUT

APN 038-050-009	Project Number	9795-26
3113 Sunnydale Dr, Napa Ca. 94558	Date	6-9-26
	Drawn By	SL
	Outkast Designs PO Box 301, Colusa CA 95632 scott@outkastdesigns.com	


S2

Scale As indicated

7/15/2026 4:41:51 PM

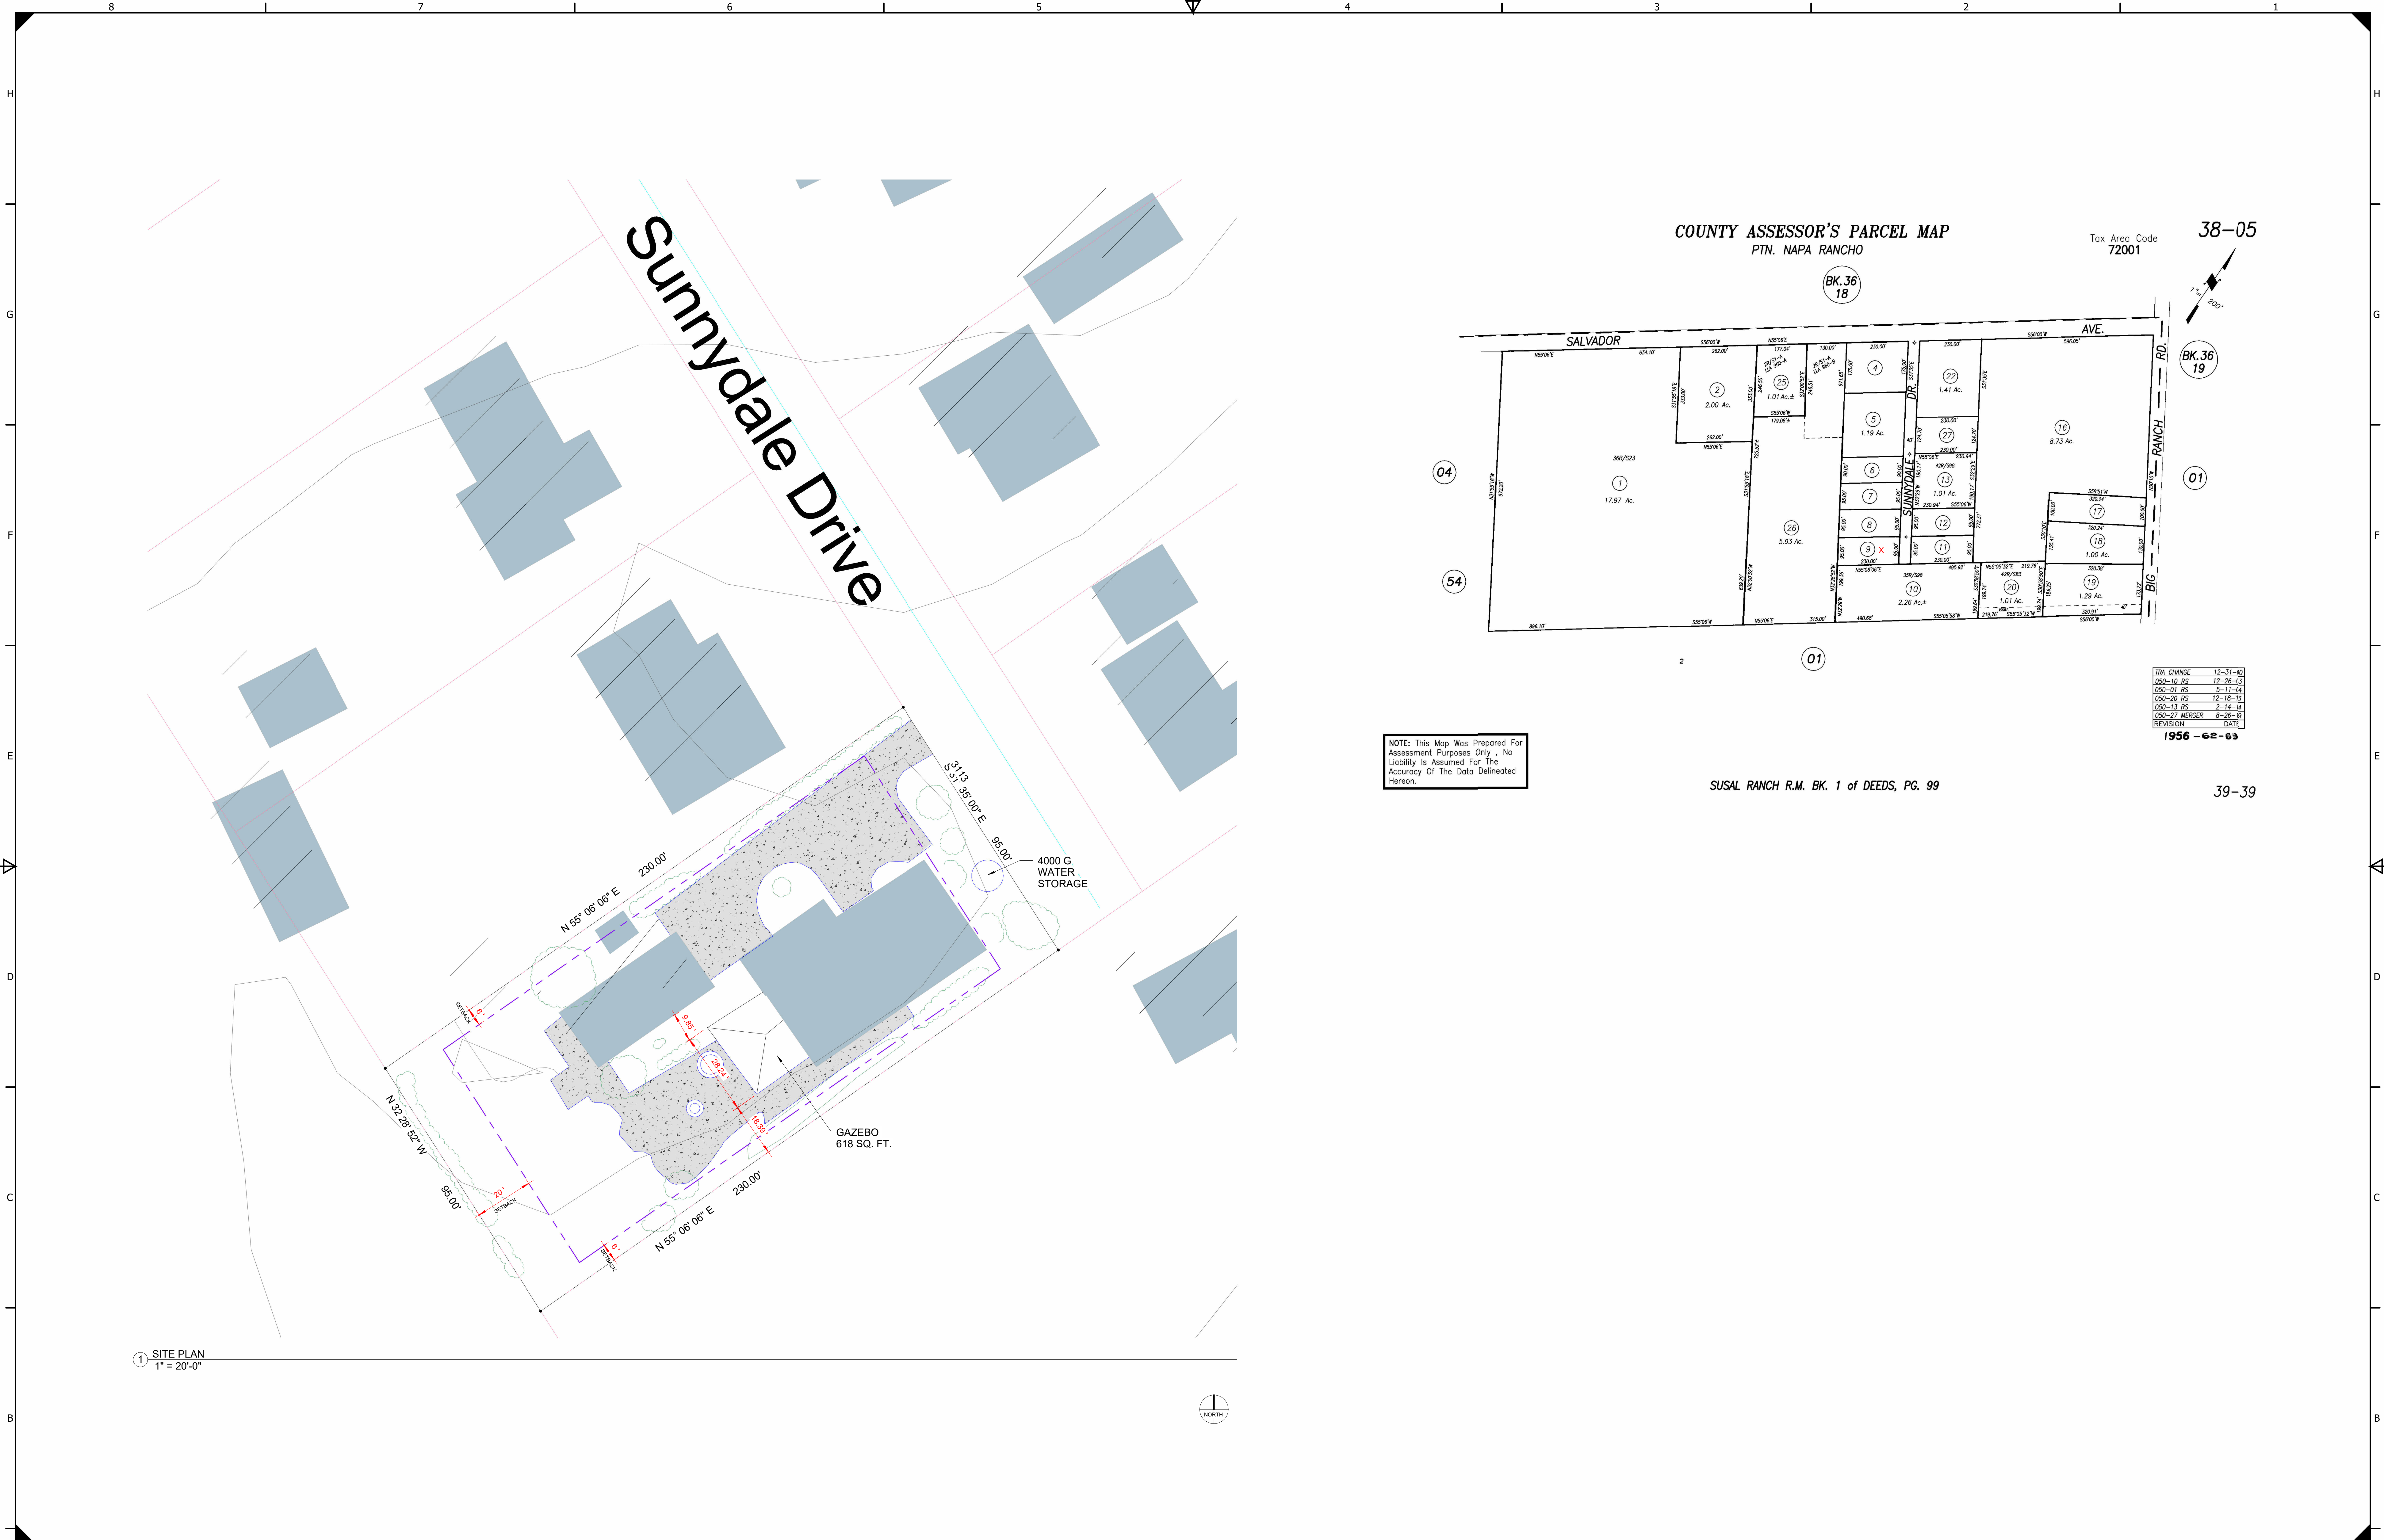

NOTE: This Map Was Prepared For
Assessment Purposes Only , No
Liability Is Assumed For The
Accuracy Of The Data Delineated
Hereon.

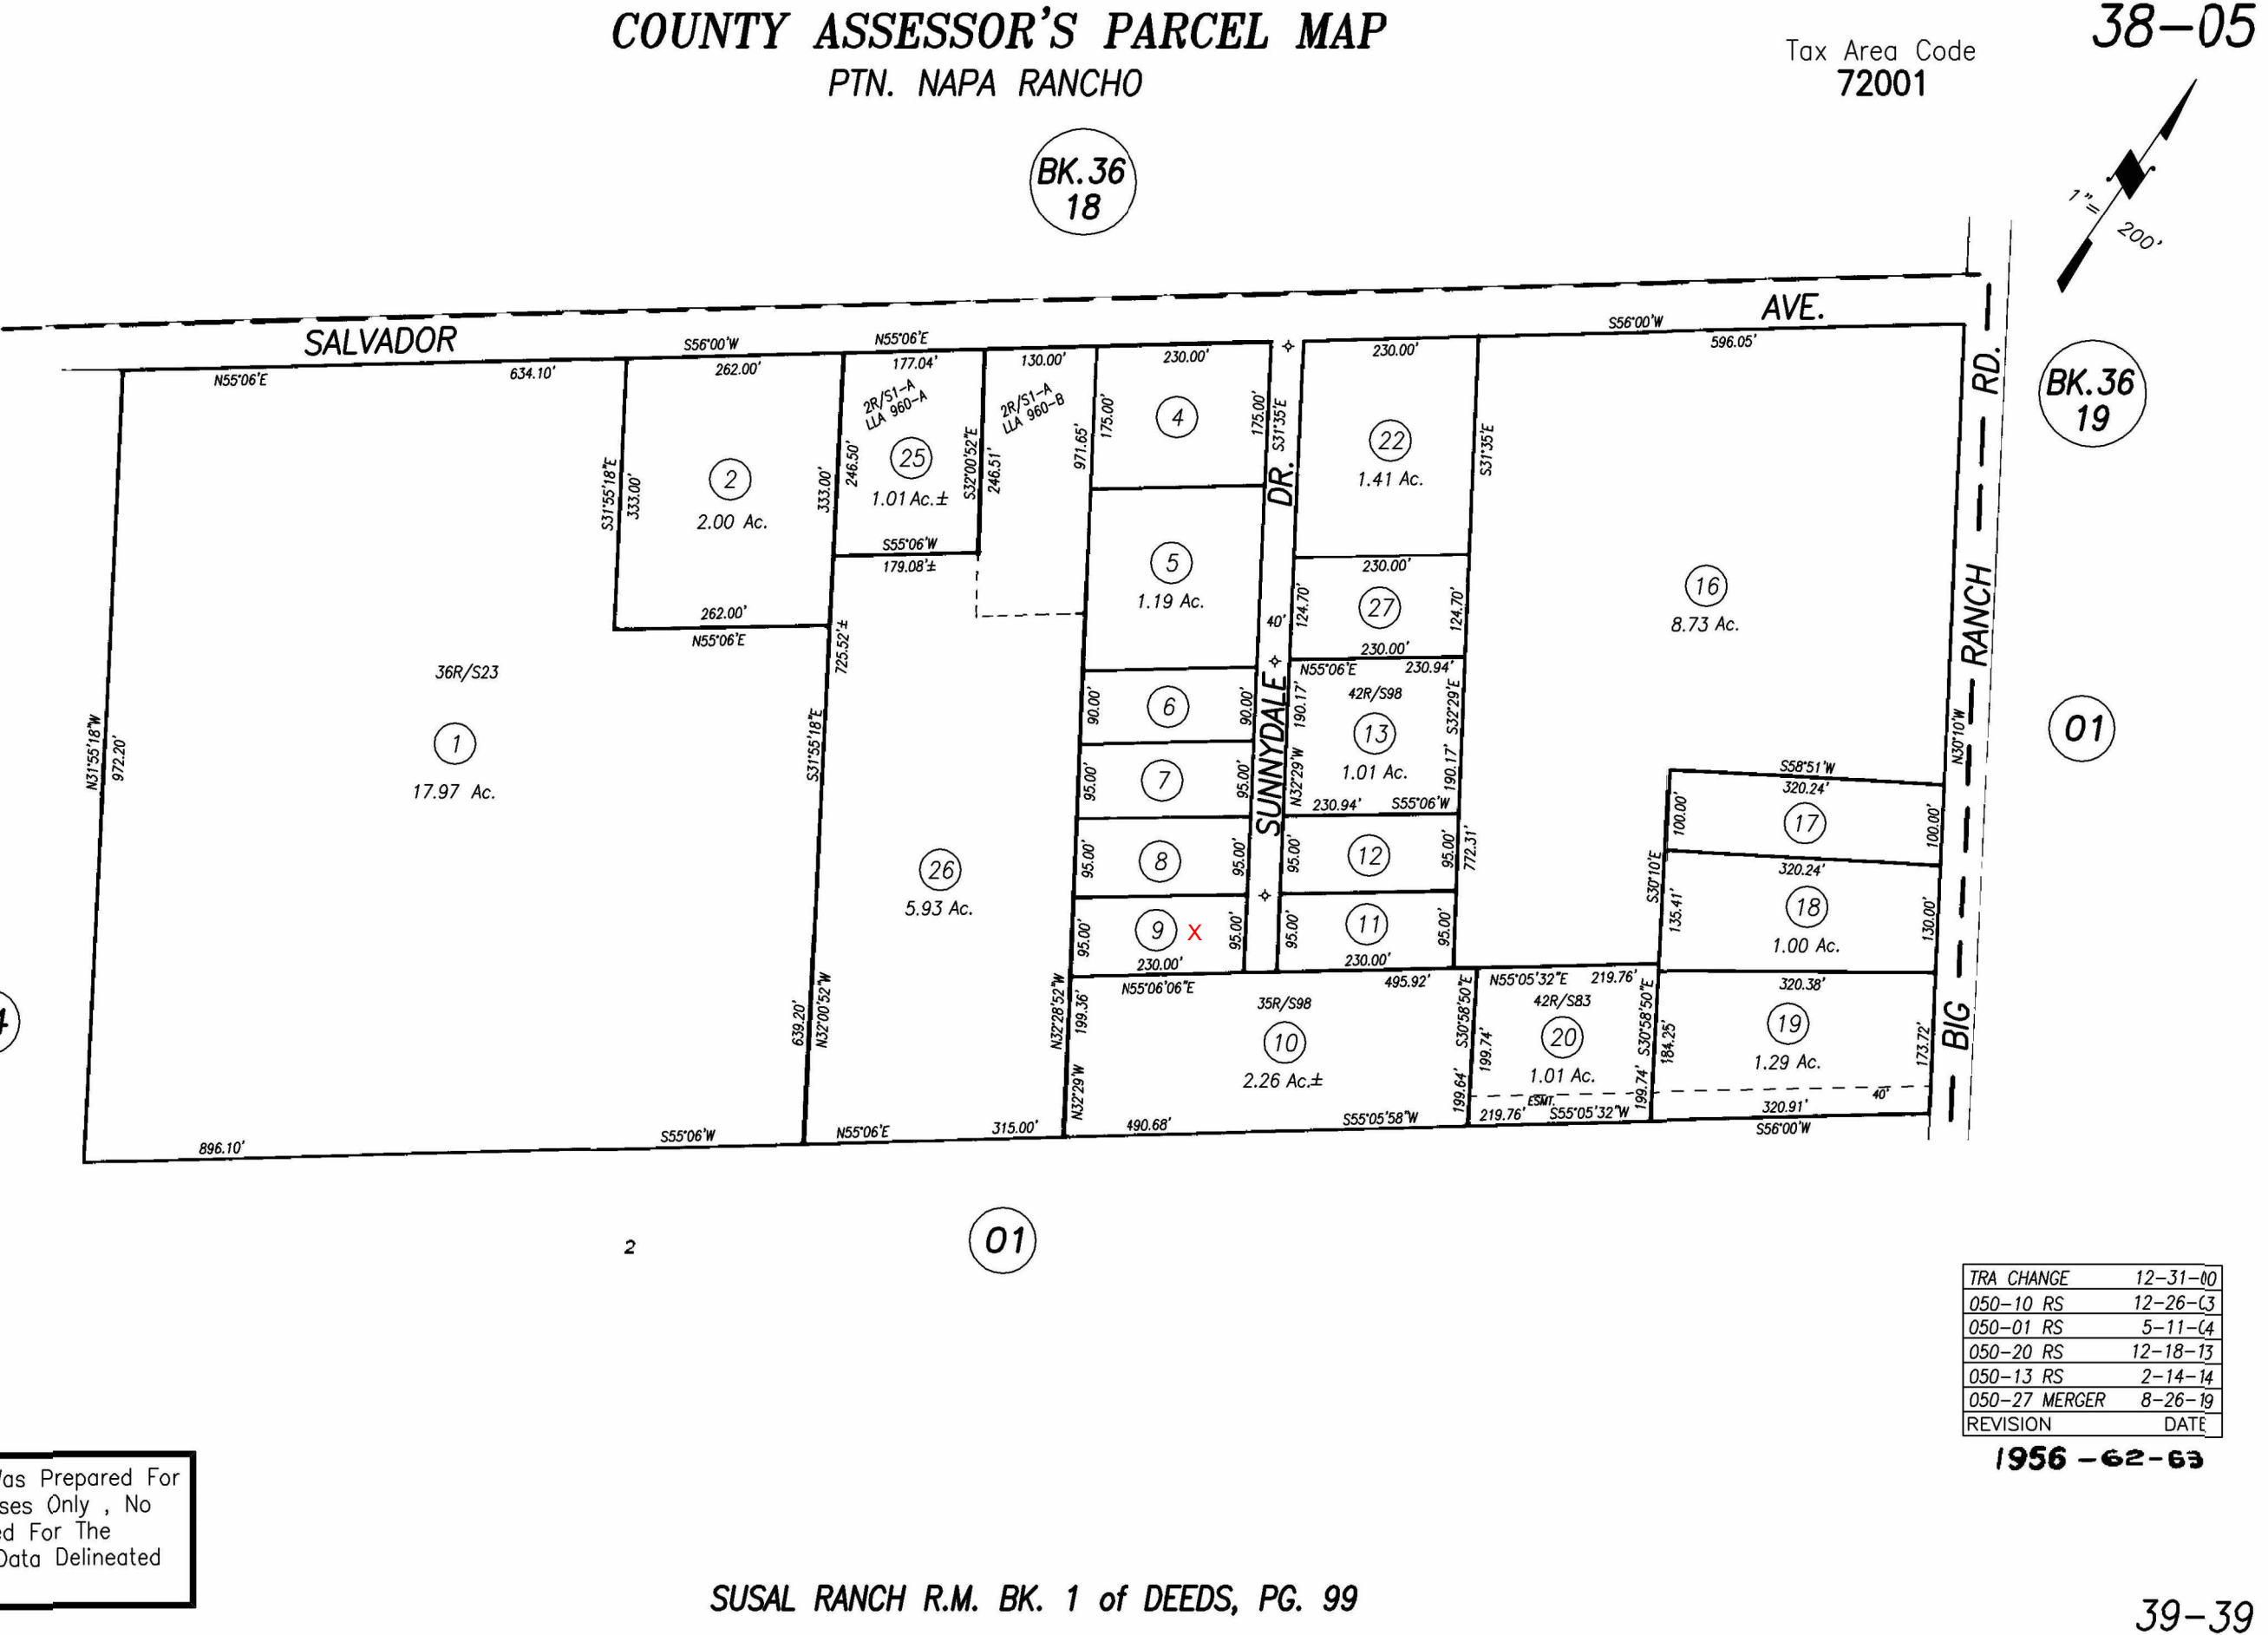



www.outkastdesigns.com

3113 SUNNYDALE



MEMBER
A I
B D
AMERICAN INSTITUTE OF
BUILDING DESIGNERS

ENGINEER OF RECORD

BUILDING DEPARTMENT

APN 038-050-009	Project Number 9795-26
3113 Sunnydale Dr, Napa Ca. 94558	Date 6-9-26
	Drawn By SL
	Outkast Designs PO Box 301 Colusa CA 95632 scott@outkastdesigns.com

C1

Scale 1" = 20'-0"

7/15/2026 4:41:56 PM